


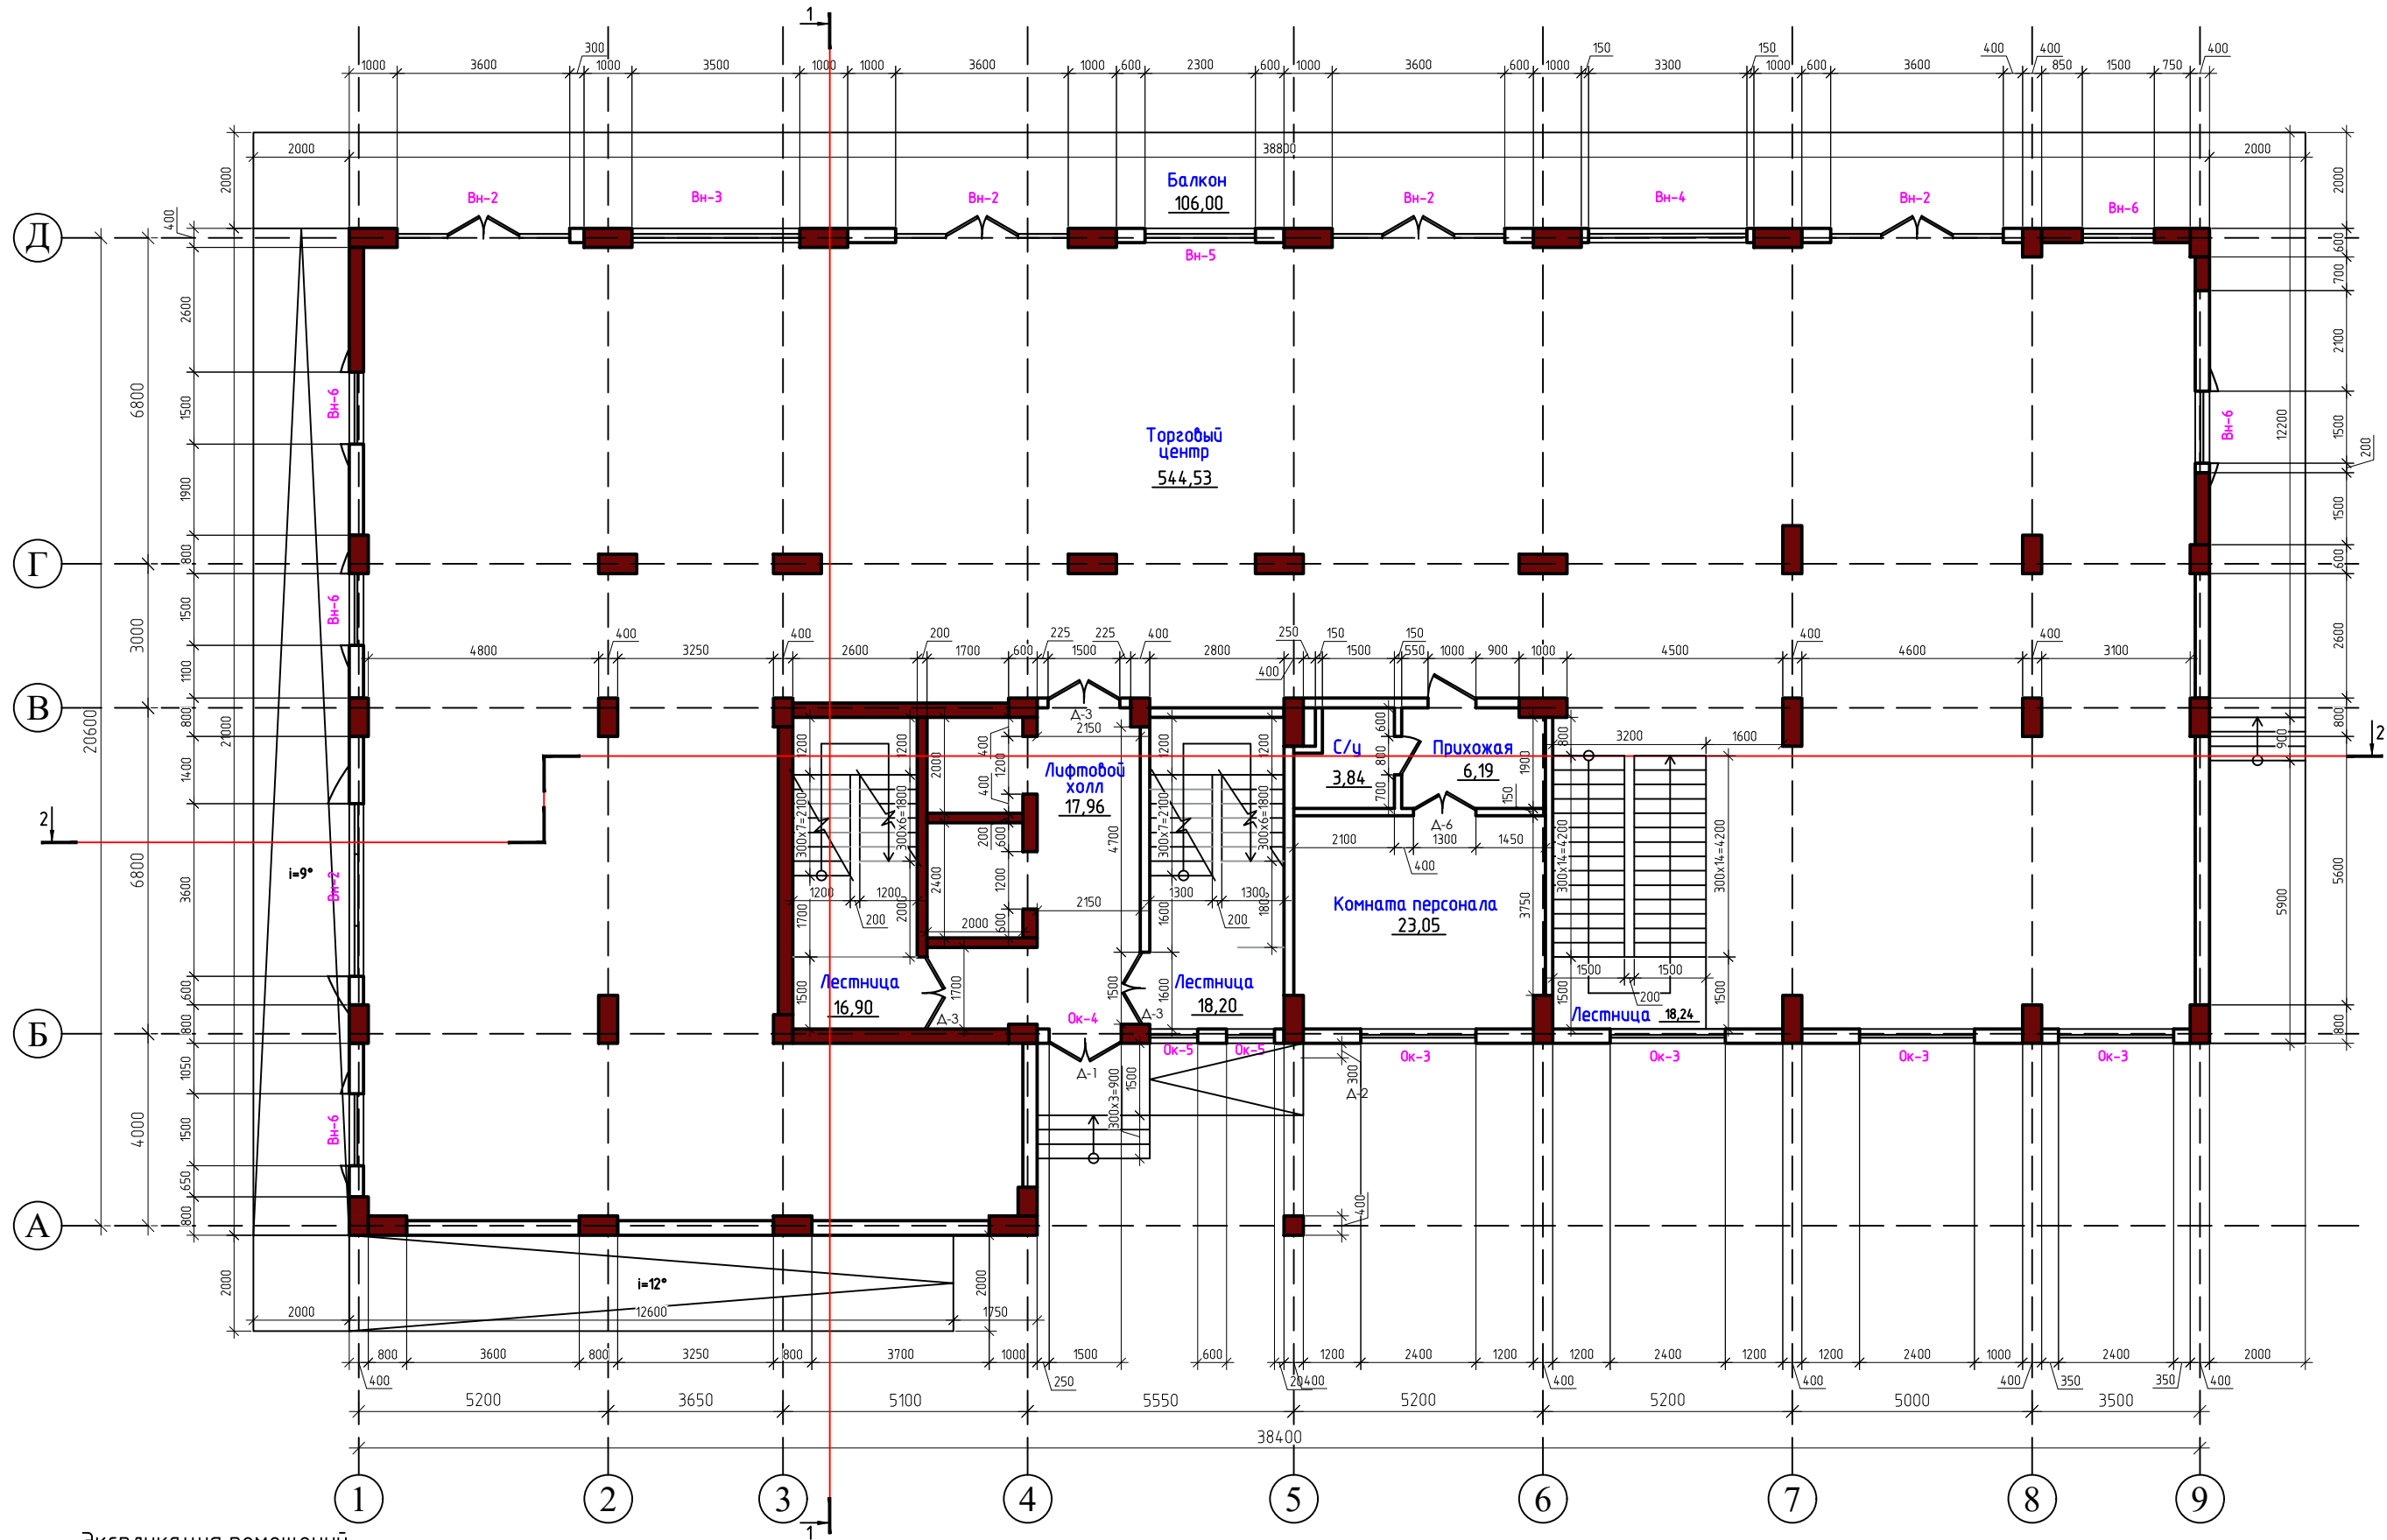

Экспликация помещений

Номер помеще-ния	Наименование	Площадь, м²	Кат. помеще-ния
1	Лифтовой холл	17.96	
2	Лестница	53.34	
3	Торговый центр	544.53	
4	Комната персонала	23.05	
5	Прихожая	6.19	
6	С/у	3.84	
7	Балкон	106.00	
	Общая площадь	754.91	

Блок А
План 1-го этажа

Изм.	Кол.уч.	Лист	№ док.	Подп.	Дата	Сохтмони биноҳои истиқомати 18,12,11 ба 9-ошёна дар ошёнаҳои якум ба дум марказҳои савдо ва хизматрасони, қудакистони замонавӣ дар дохили биноҳои истиқомати, дар зери биноҳои таваккуфҳои нақлиётӣ сабққараби 2-ошёнаги, дар назди биноҳои майдончаҳои бозии дачагона ба ҷои дамғири калонсолон			
						Фармоишгар: "Элит Сохтмон"	Ставия	Лист	Листов
						План 1-го этажа	рп	5	35
Иҷро кард	Шарипов А								