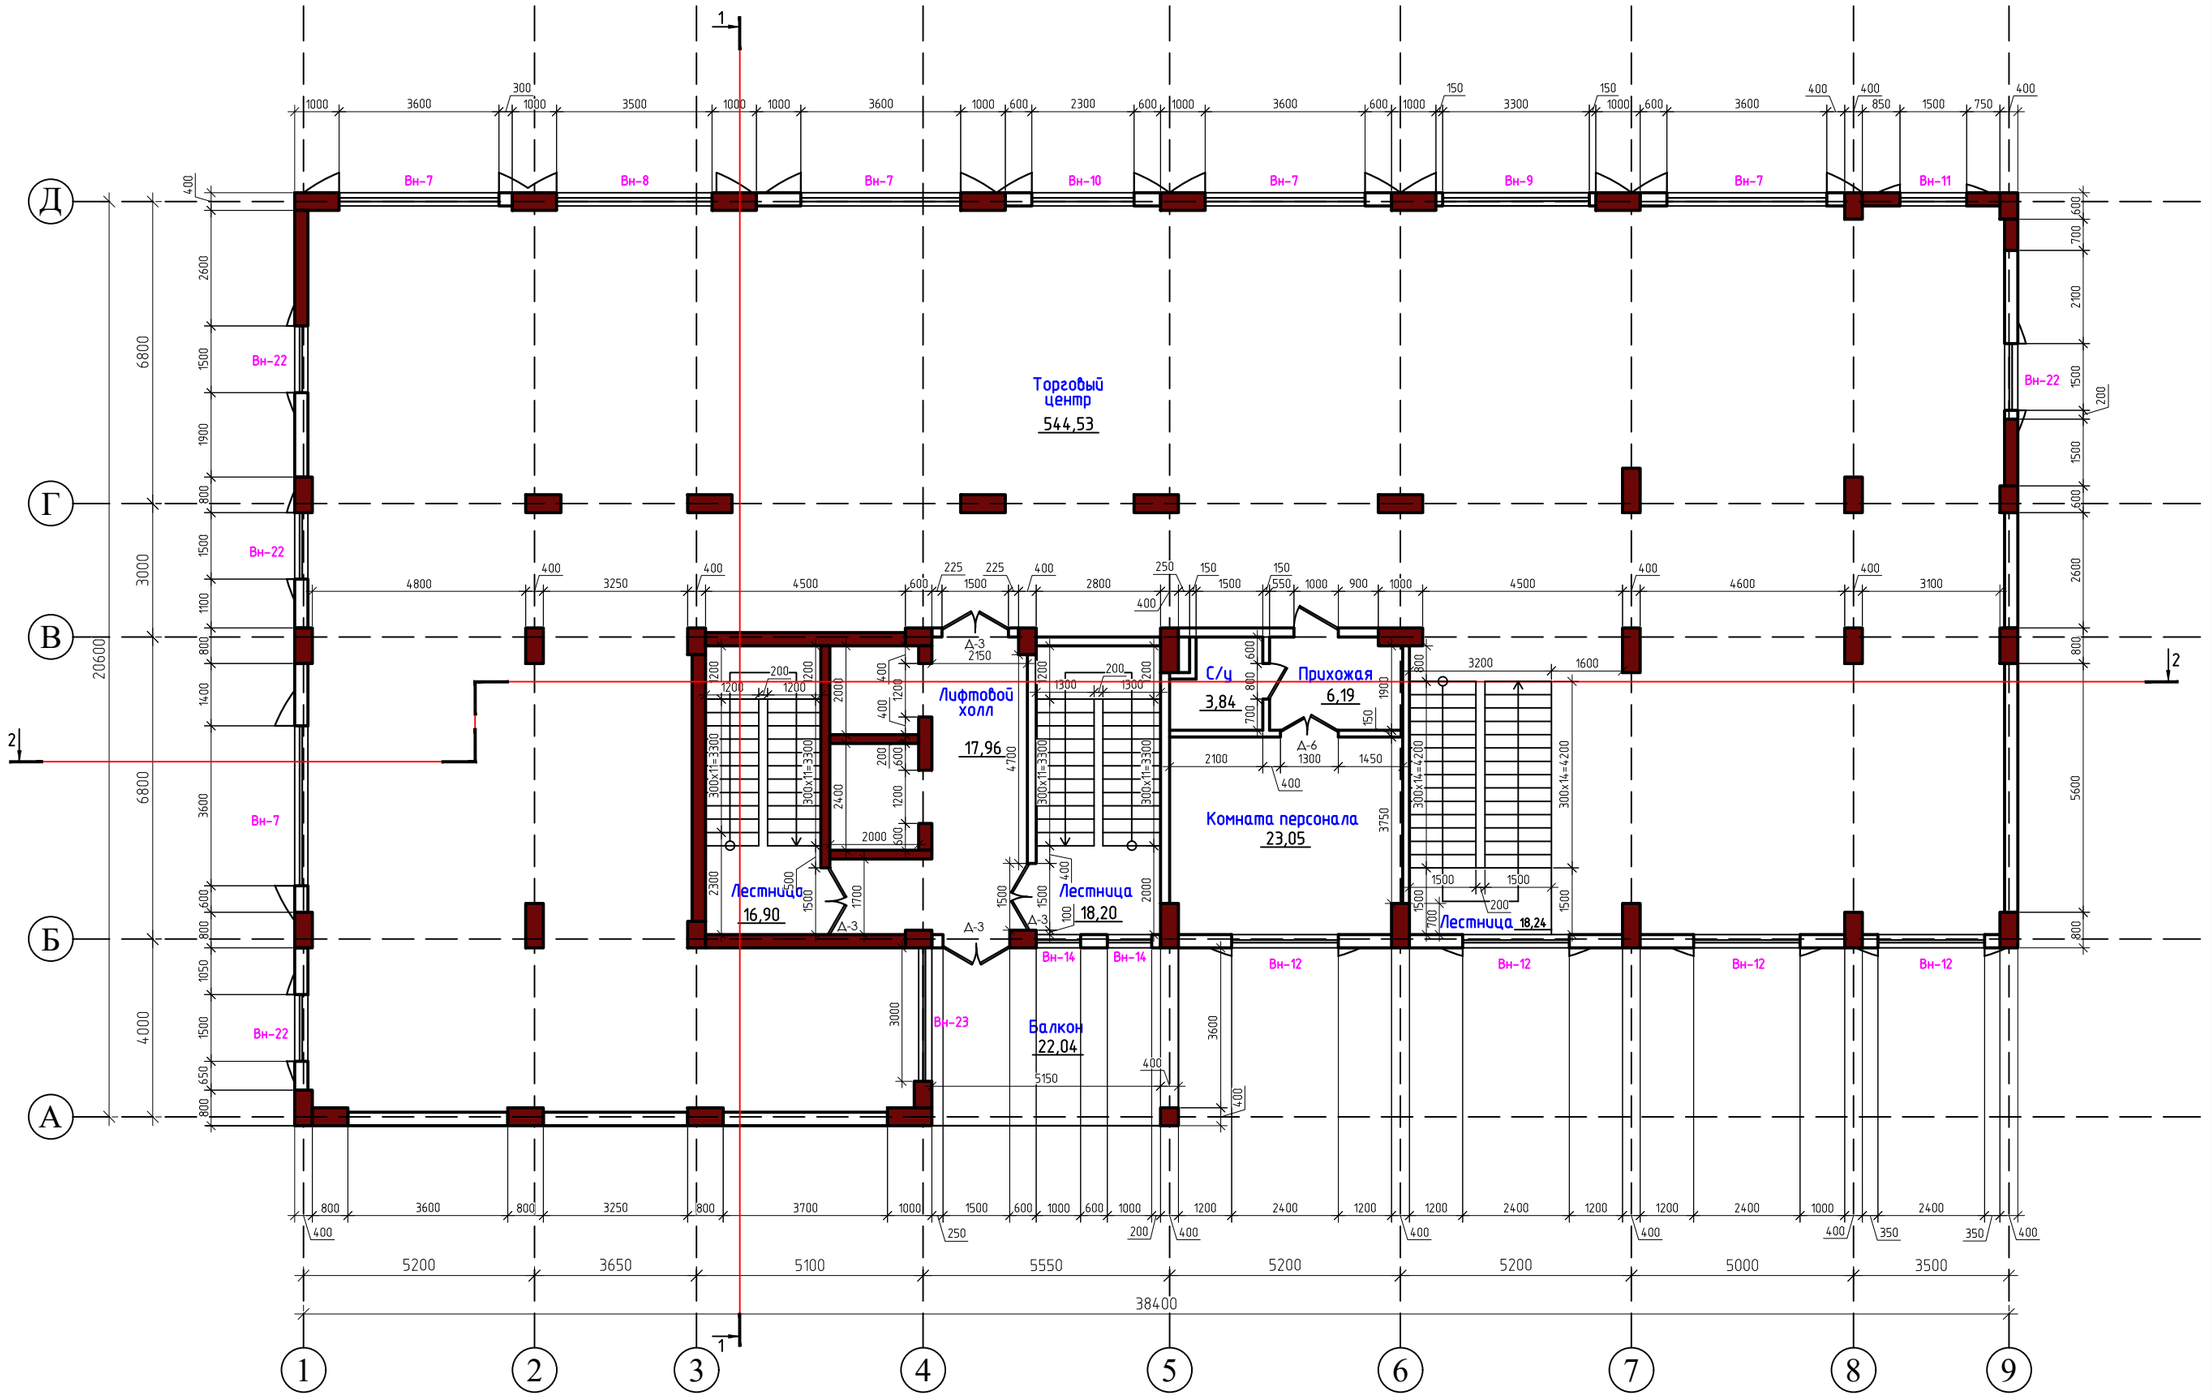



Экспликация помещений

| Номер помещения | Наименование | Площадь, м² | Кат.* помещения |
|---|---|---|---|
| 1 | Лифтовой холл | 17.96 | |
| 2 | Лестница | 53,34 | |
| 3 | Торговый центр | 544,53 | |
| 4 | Комната персонала | 23,05 | |
| 5 | Прихожая | 6,19 | |
| 6 | С/у | 3,84 | |
| 7 | Балкон | 22,04 | |
| | Общая площедь | 670.95 | |

# Блок А
# План 2-го этажа

| Изм. | Кол.уч. | Лист | № док. | Подп. | Дата | Сохтмони бинохои истикоматии 18,12,11 ва 9-ошёна дар ошёнахои якум ва дуюм марказхои савдо ва хизматрасони, кудакистони замонави дар бохили бинои истикомати, дар зери бинохо тавакқуфгохи наклиёти сайёкравй 2-ошёнаги, дар назди бинохо майдончахои бозии бачагона ва чои дамгирии калонсолон | | | |
|---|---|---|---|---|---|---|---|---|---|
| | | | | | | Фармоишгар: "Элит Сохтмон" | Стадия | Лист | Листов |
| | | | | | | | РП | 6 | 35 |
| | | | | | | План 2-го этажа | ЧДММ "АРК СИНОН" | | |
| Ичро кард | | Шарипов А | | | | | | | |