



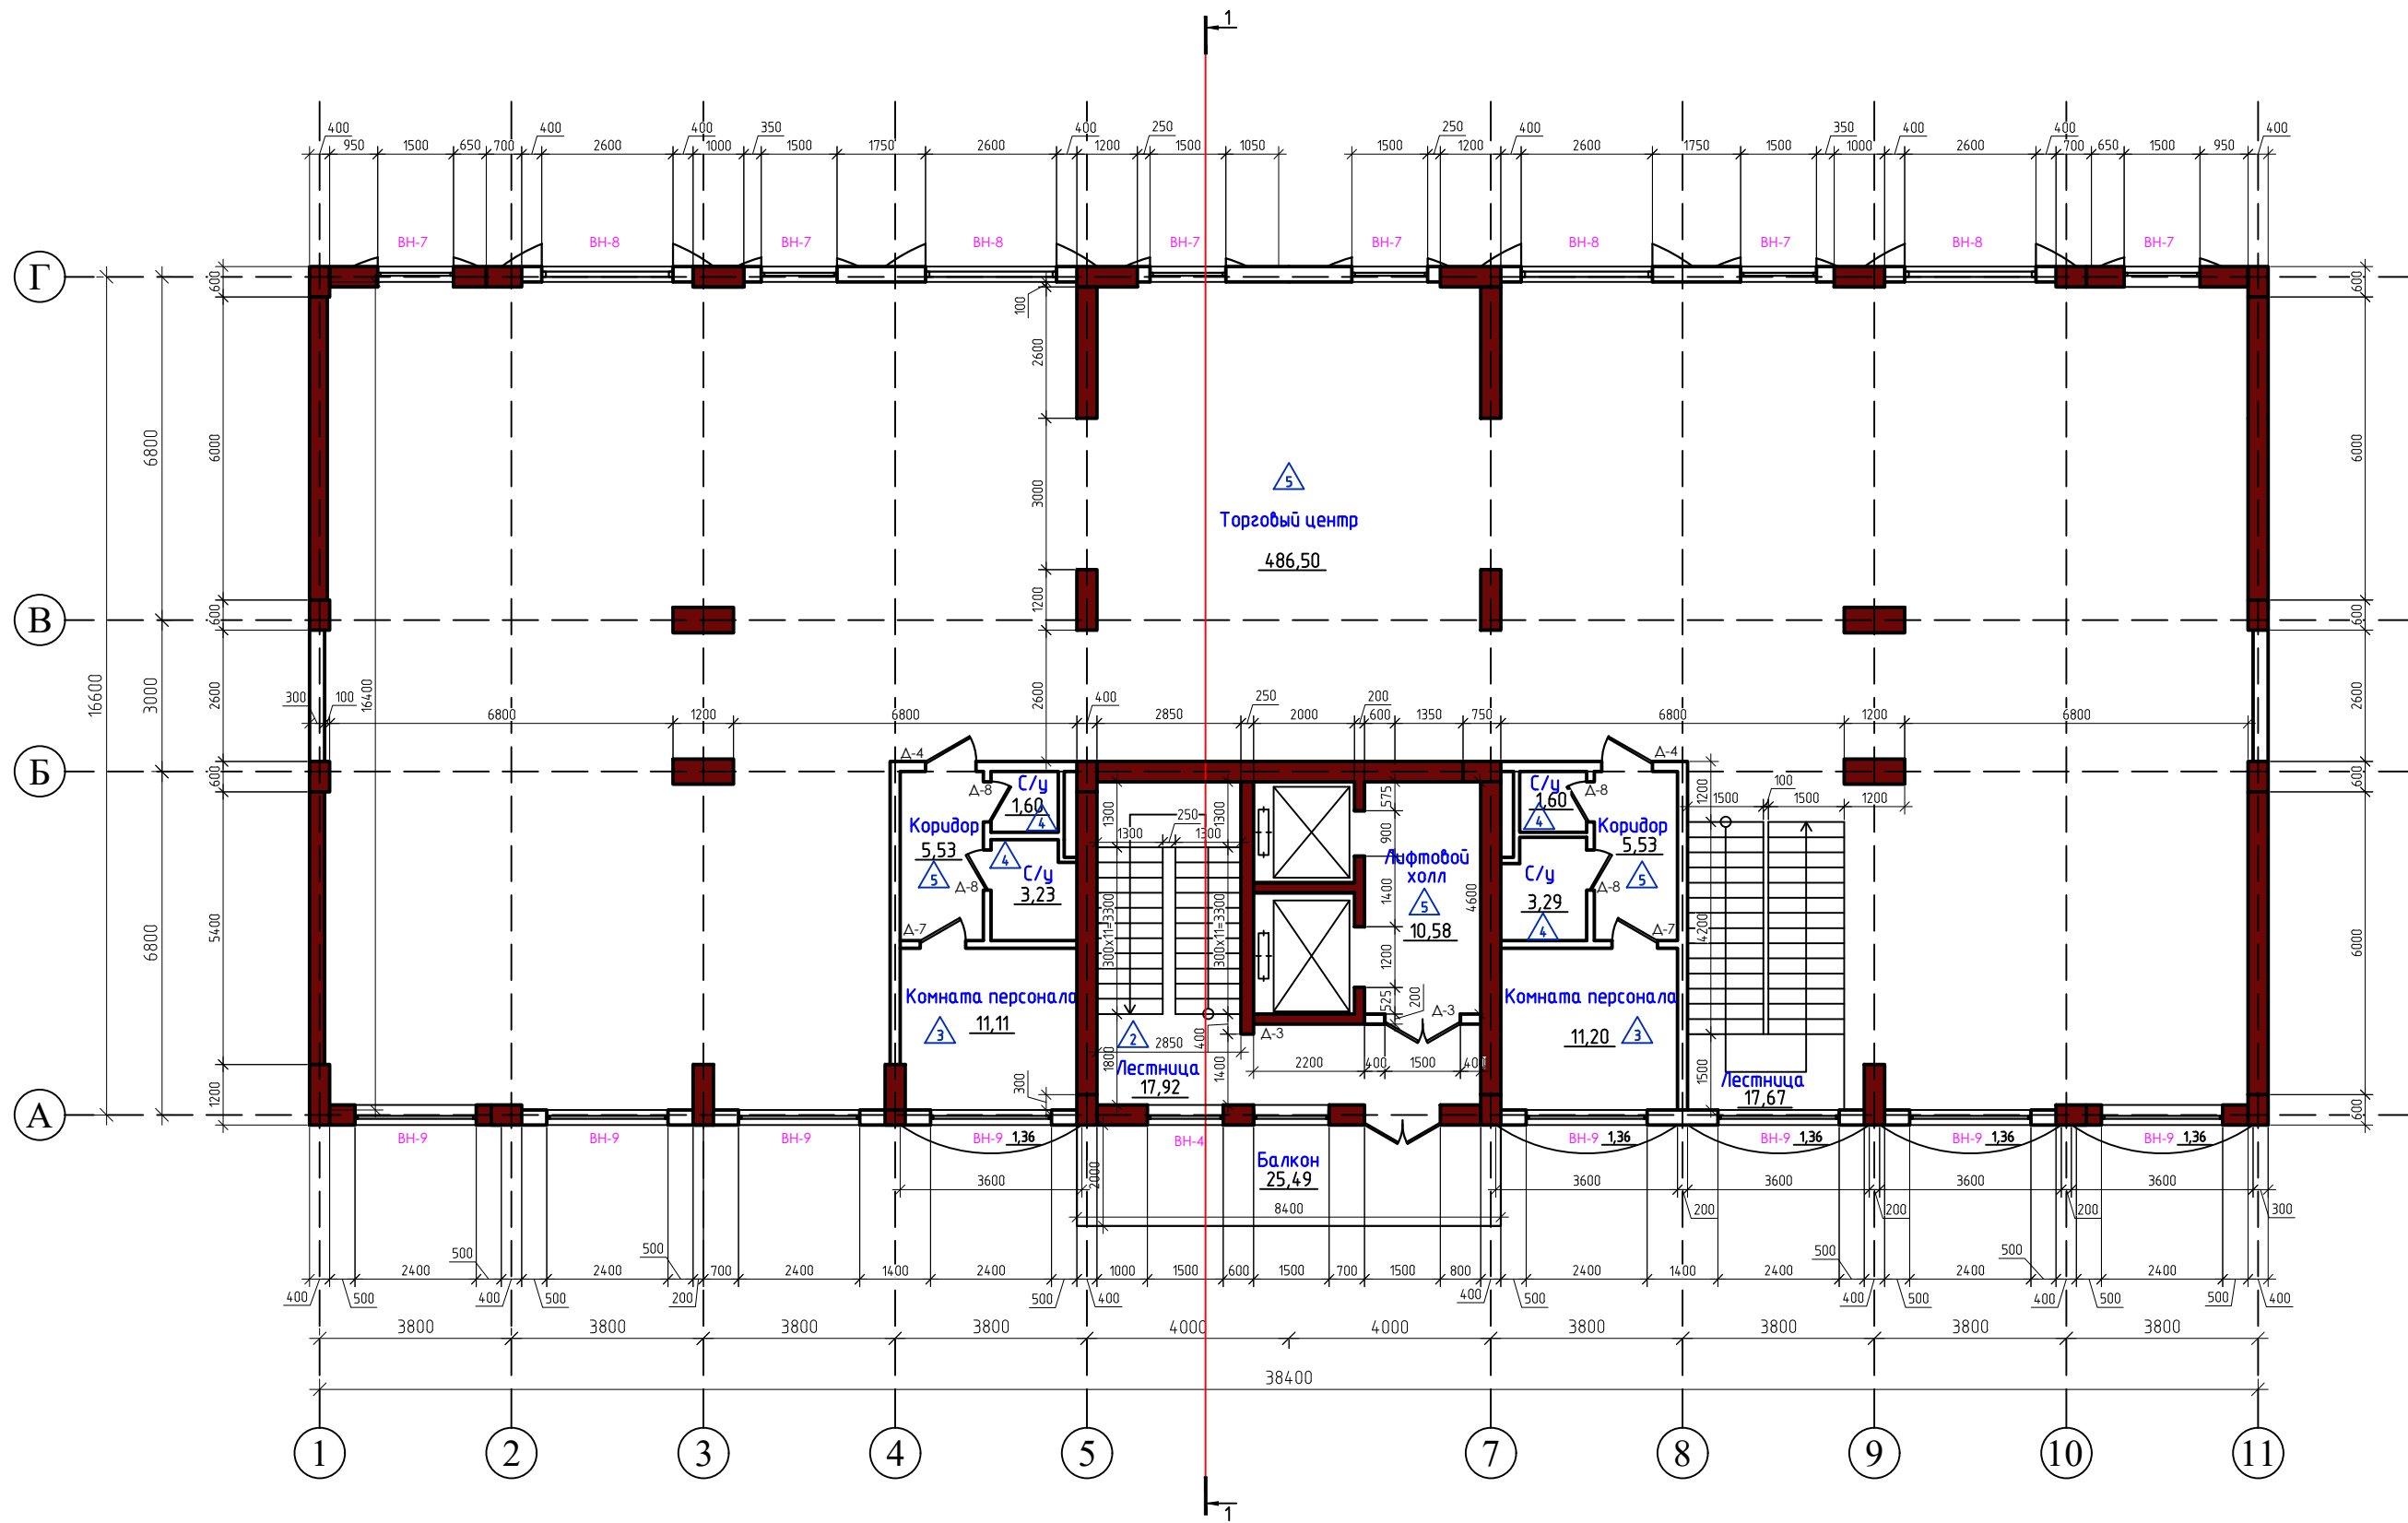

Экспликация помещений

Номер помеще-ния	Наименование	Площадь, м²	Кат. помеще-ния
1	Лифтовой холл	10.58	
2	Лестница	35.59	
3	Коридор	11.06	
4	Комната персонала	22.31	
5	Торговый центр	486.50	
6	Балкон	32.29	
7	Ванная	6.52	
8	Санузел	3.2	
	Общая площадь	608.05	

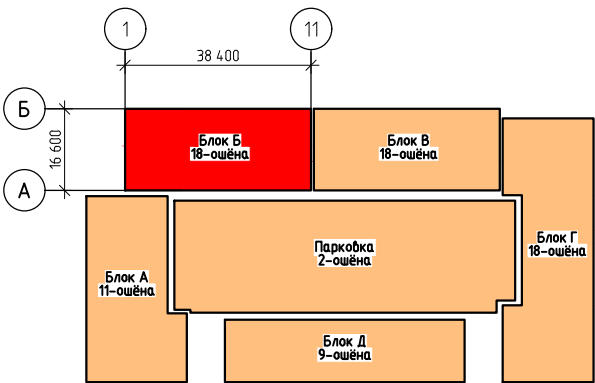

Изм.	Кол.уч.	Лист	№ док.	Подп.	Дата	Сохтмони биноҳои истиқоматии 18,12,11 ва 9-ошёна дар ошёнаҳои якум ва дуюм марказҳои савдо ва хизматрасони, қудакистони замонавӣ дар дохили биноҳои истиқоматӣ, дар зери биноҳои табаккуфгоҳи нақлиётӣ садқабраи 2-ошёнаги, дар назди биноҳои майдончаҳои бозии дачагона ва ҷои дамгузри калонсолон			
						Фармоишгар: "Элит Сохтмон"			
						План 2-го этажа Отм. (+4,500)			
						Ч ДММ "АРК СИНОН"			
Иҷро кард	Шарипов А					Ставия	Лист	Листов	
						рп	6	31	