



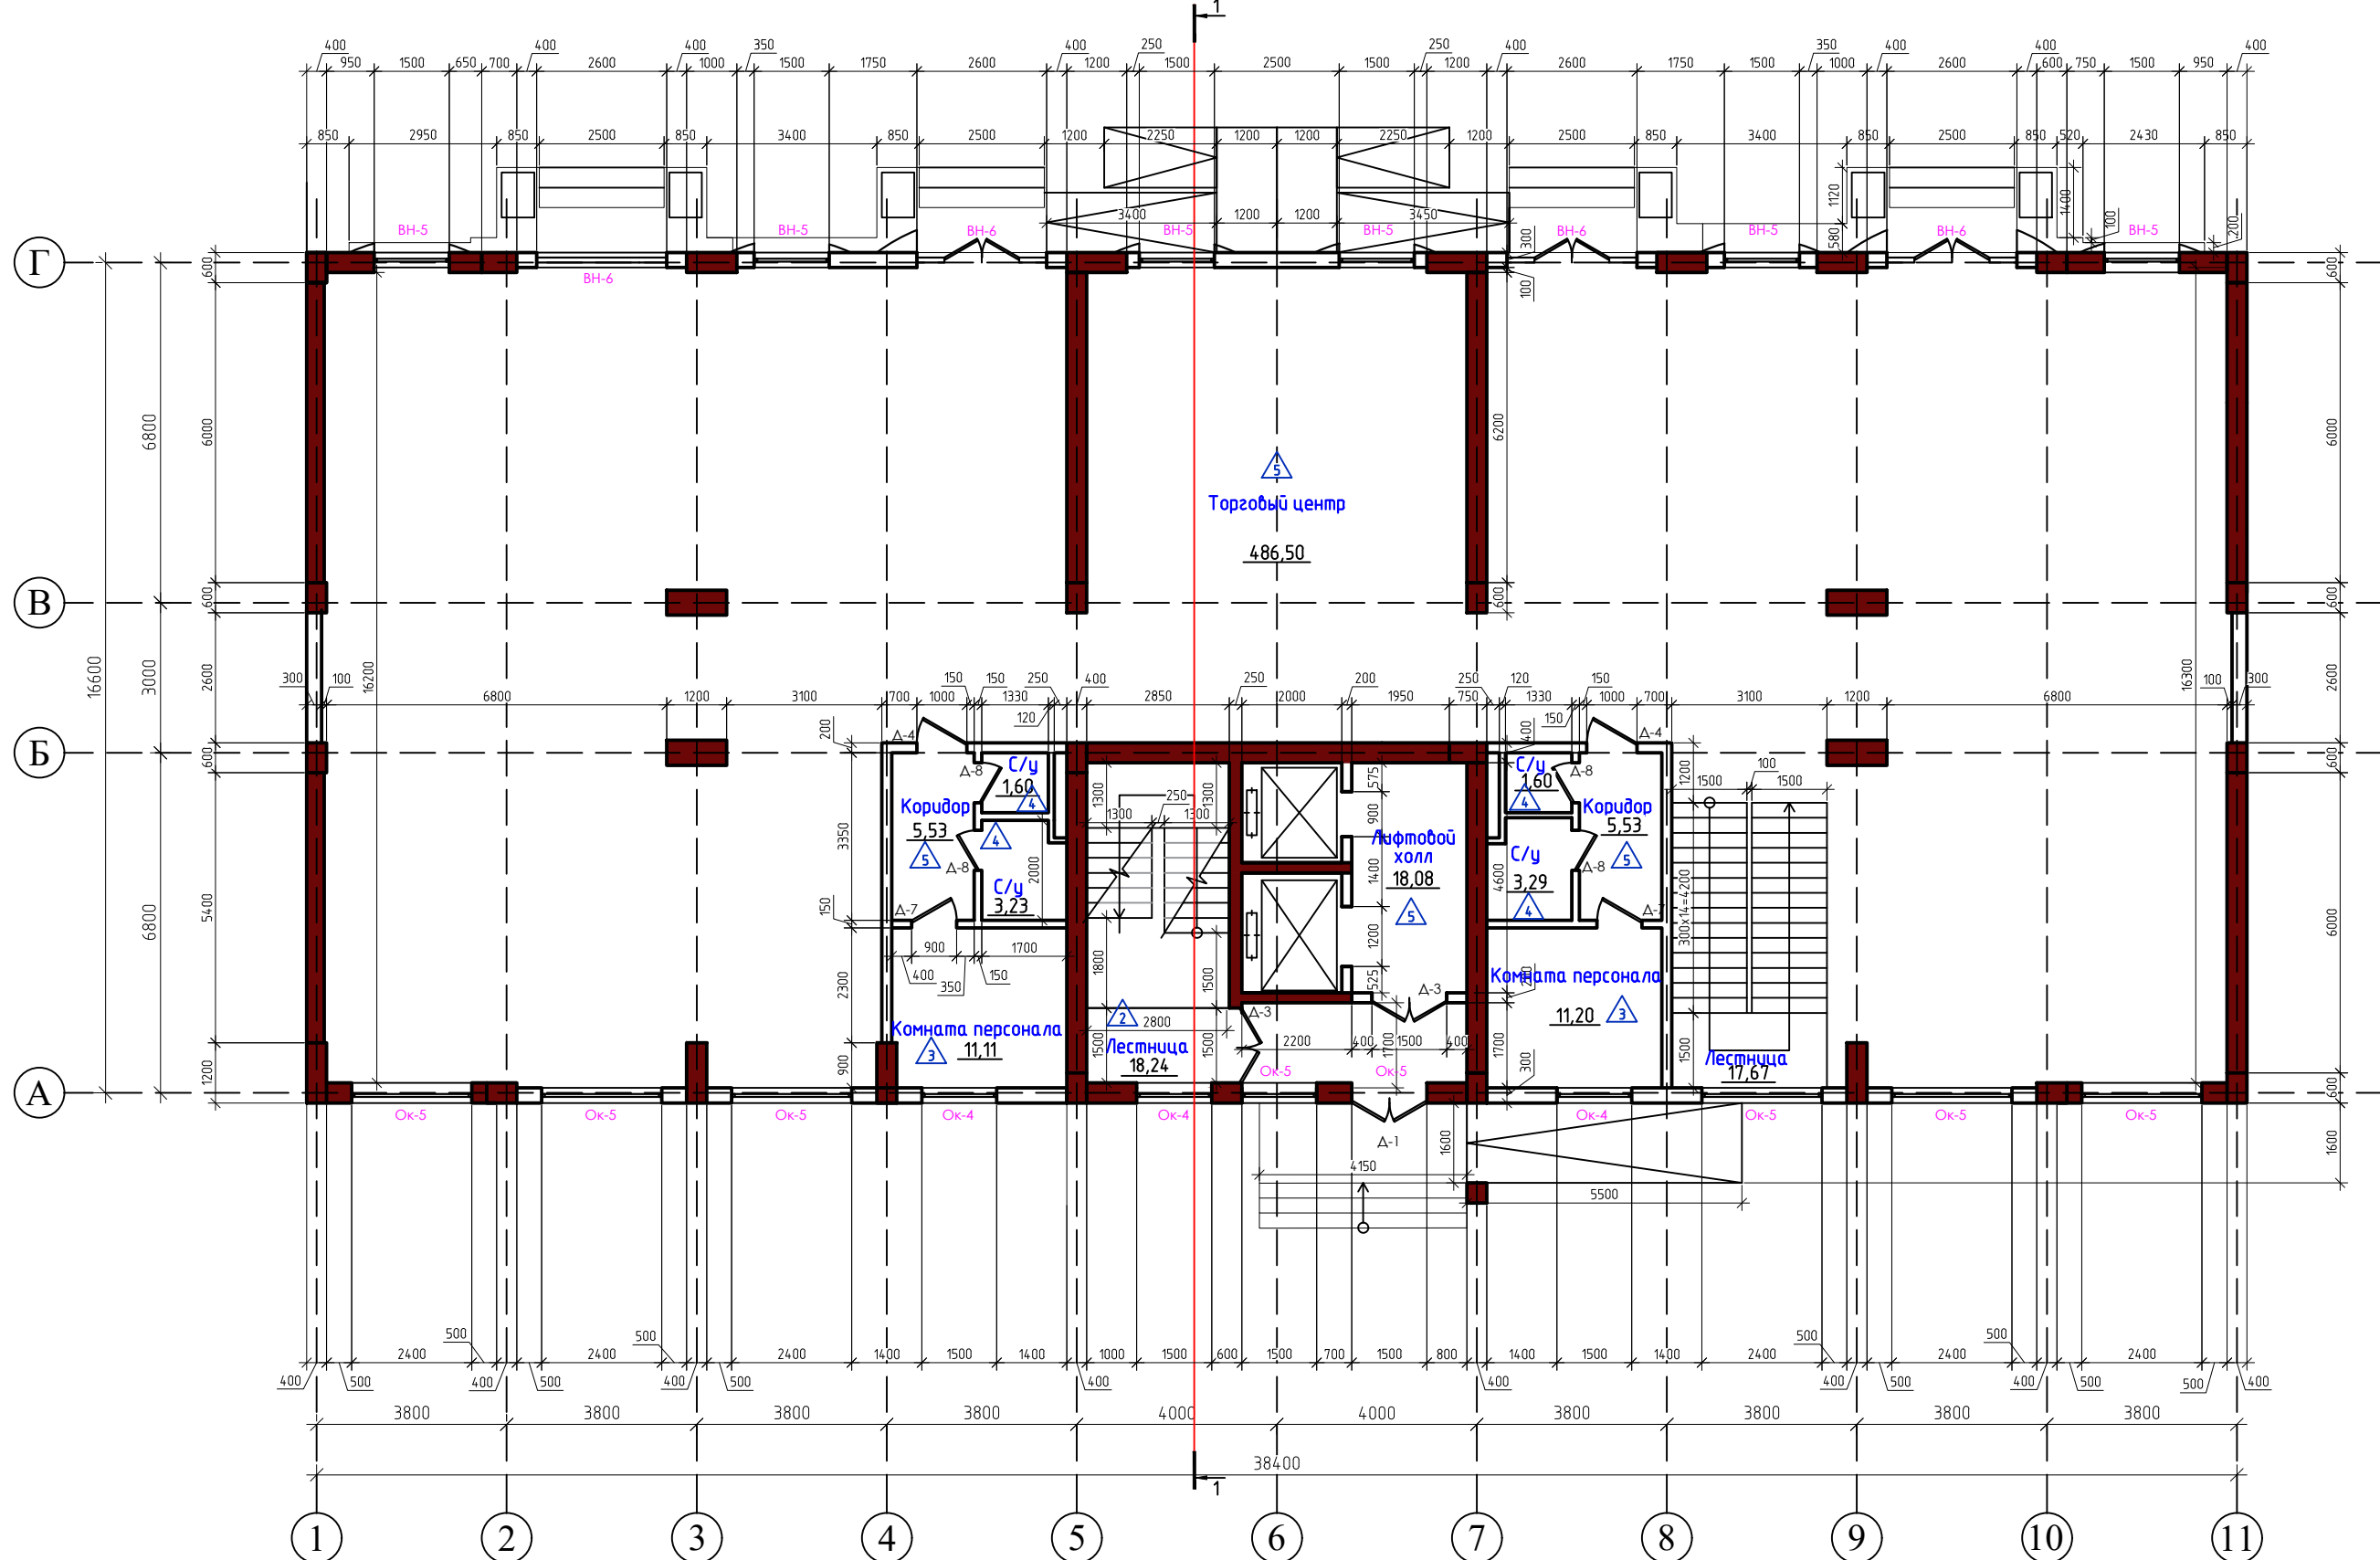

Экспликация помещений

Номер помеще-ния	Наименование	Площадь, м²	Кат. помеще-ния
1	Лифтовой холл	18,08	
2	Лестница	35,91	
3	Коридор	11,06	
4	Комната персонала	22,31	
5	Торговый центр	486,50	
7	Ванная	6,52	
8	Санузел	3,2	
	Общая площадь	583,58	

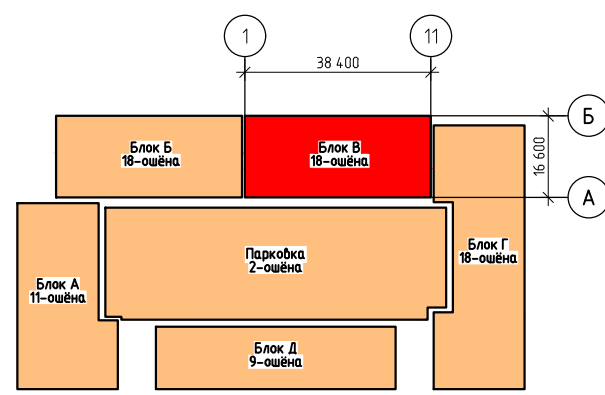

Изм.	Кол.уч.	Лист	№ док.	Подп.	Дата	Сохтмони биноҳои истиқоматии 18,12,11 ва 9-ошёна дар ошёнаҳои якум ва дуюм марказҳои савдо ва хизматрасони, қудрати қувватҳои замонавӣ дар дохили биноҳои истиқоматӣ, дар зери биноҳои таваққуфҳои нақлиётӣ сабққарабӣ 2-ошёнагӣ, дар назди биноҳои майдонҳои бозии дачагона ва ҷои дамҷури калонсолон			
						Фармоишгар: "Элит Сохтмон"			
						План 1-го этажа Омм. (0,000)			
						Ч ДММ "АРК СИНОН"			
Иҷро кард	Шарипов А					РП	5	31	